PIANTA — PIANO PRIMO · STATO COMPARATIVO

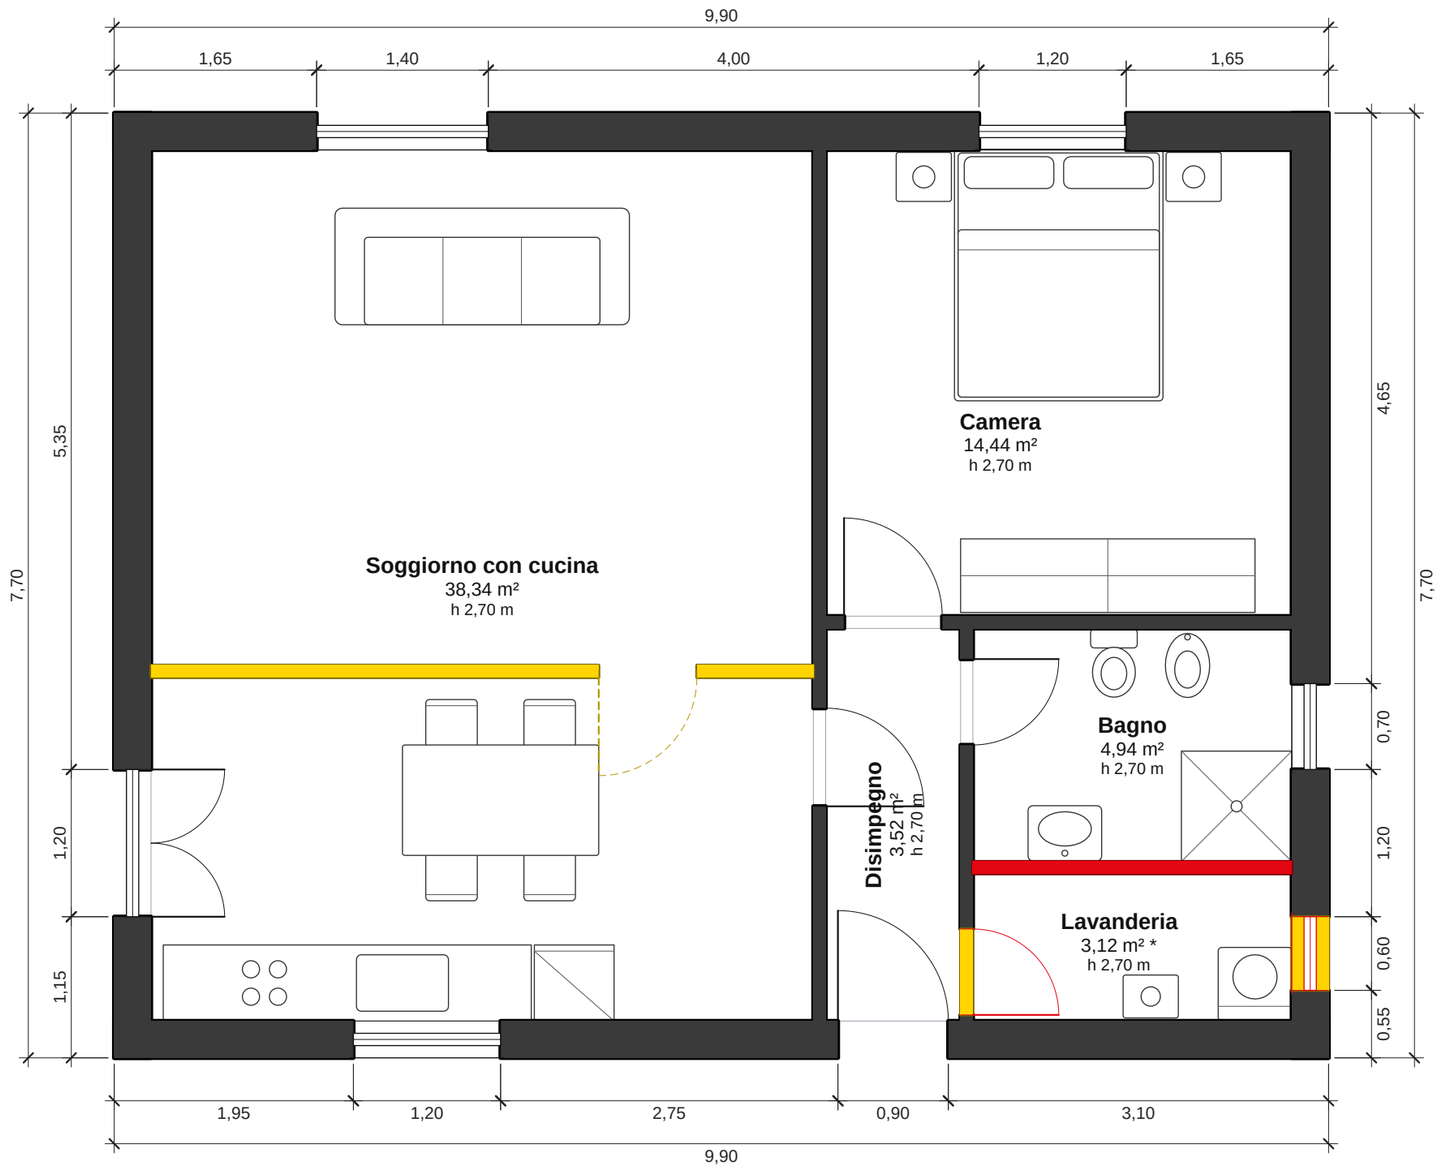

LEGENDA

- Muri esistenti
- Demolizioni (giallo)
- Nuove costruzioni (rosso)

LOCALI

Locale	Sup. m²	Perim. m	H m
Soggiorno con cucina	38,34	25,00	2,70
Camera	14,44	15,20	2,70
Disimpegno	3,52	8,60	2,70
Bagno	4,94	9,00	2,70
Lavanderia *	3,12	7,60	2,70
Totale	**64,36**		

* misura stimata, da verificare sul posto

Scala 1:50

0 — 0,5 — 1 — 1,5 — 2 — 2,5 m

Stampare al 100%,
senza «adatta alla pagina».
1 cm sul foglio = 0,50 m in cantiere.

Edil Rossi S.r.l.
Via dei Mille 8, 20121 Milano (MI)
P.IVA 01234567890 · 02 1234567
ufficio@edilrossi.it

OGGETTO
Appartamento via Roma 12 — Stato comparativo (demolizioni e nuove c…

CLIENTE
Mario Bianchi

CANTIERE
Via Roma 12, 20900 Monza (MB) — interno 4

SCALA	FORMATO	DATA	VERSIONE	TAVOLA
1:50	A3	30/10/2026	v3	1/1